



## EJIDO LEONA VICARIO MUNICIPIO: PUERTO MORELOS,

ESTADO: QUINTANA ROO.

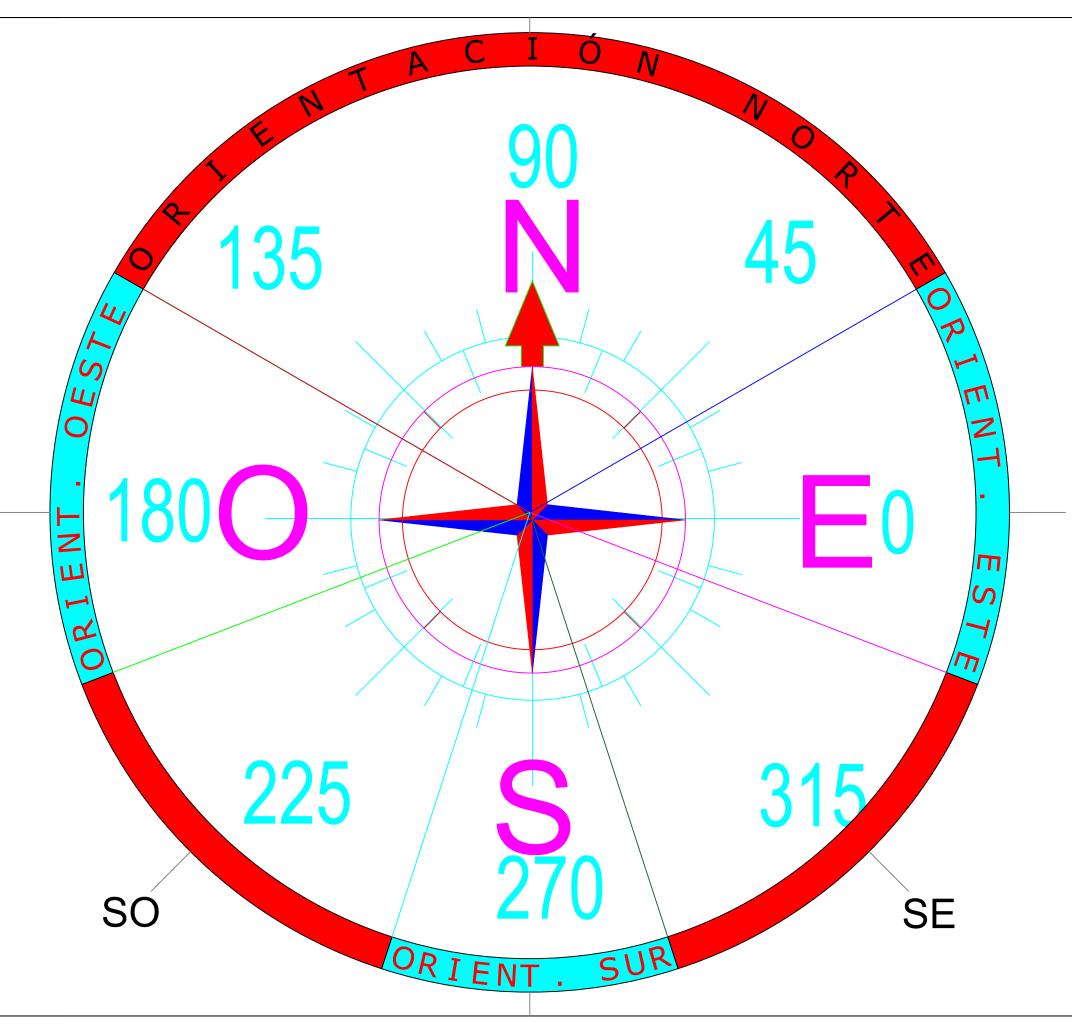

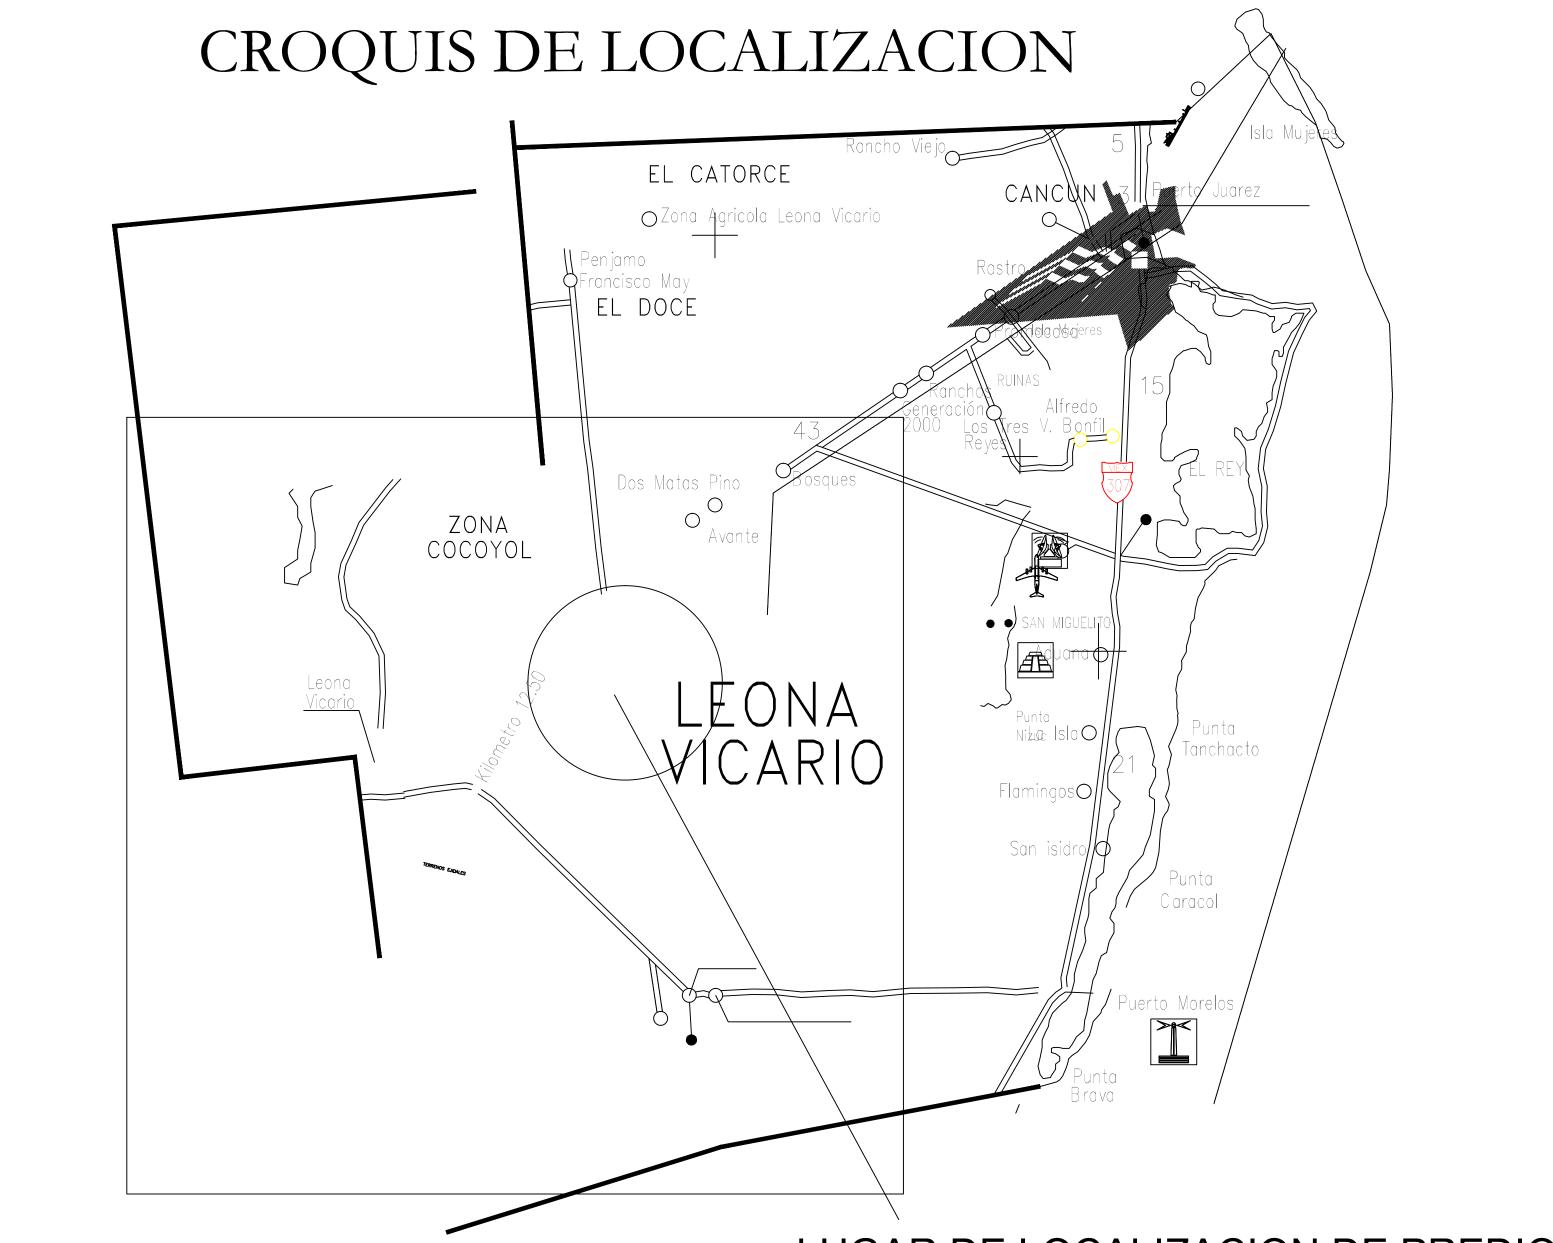

UBICACION: EJIDO LEONA VICARIO

TERRENO: PARCELA
TIPO DE PLANO: TOPOGRÁFICO

N° DE PLANO:

POSESIONARIO

SUPERFICIE:

FECHA DE ELABORACION:

10 DE JUNIO DEL 2020

EL NORTE ES GEOGRAFICO

2.- EL SISTEMA DE COORDENADAS ES UTM DATUM WGS 84

IDENTIFICACION GEOGRAFICA

QUINTANA ROO

PUERTO MORELOS
LEONA VICARIO

RESPONSABLE DEL LEVANTAMIENTO:

